



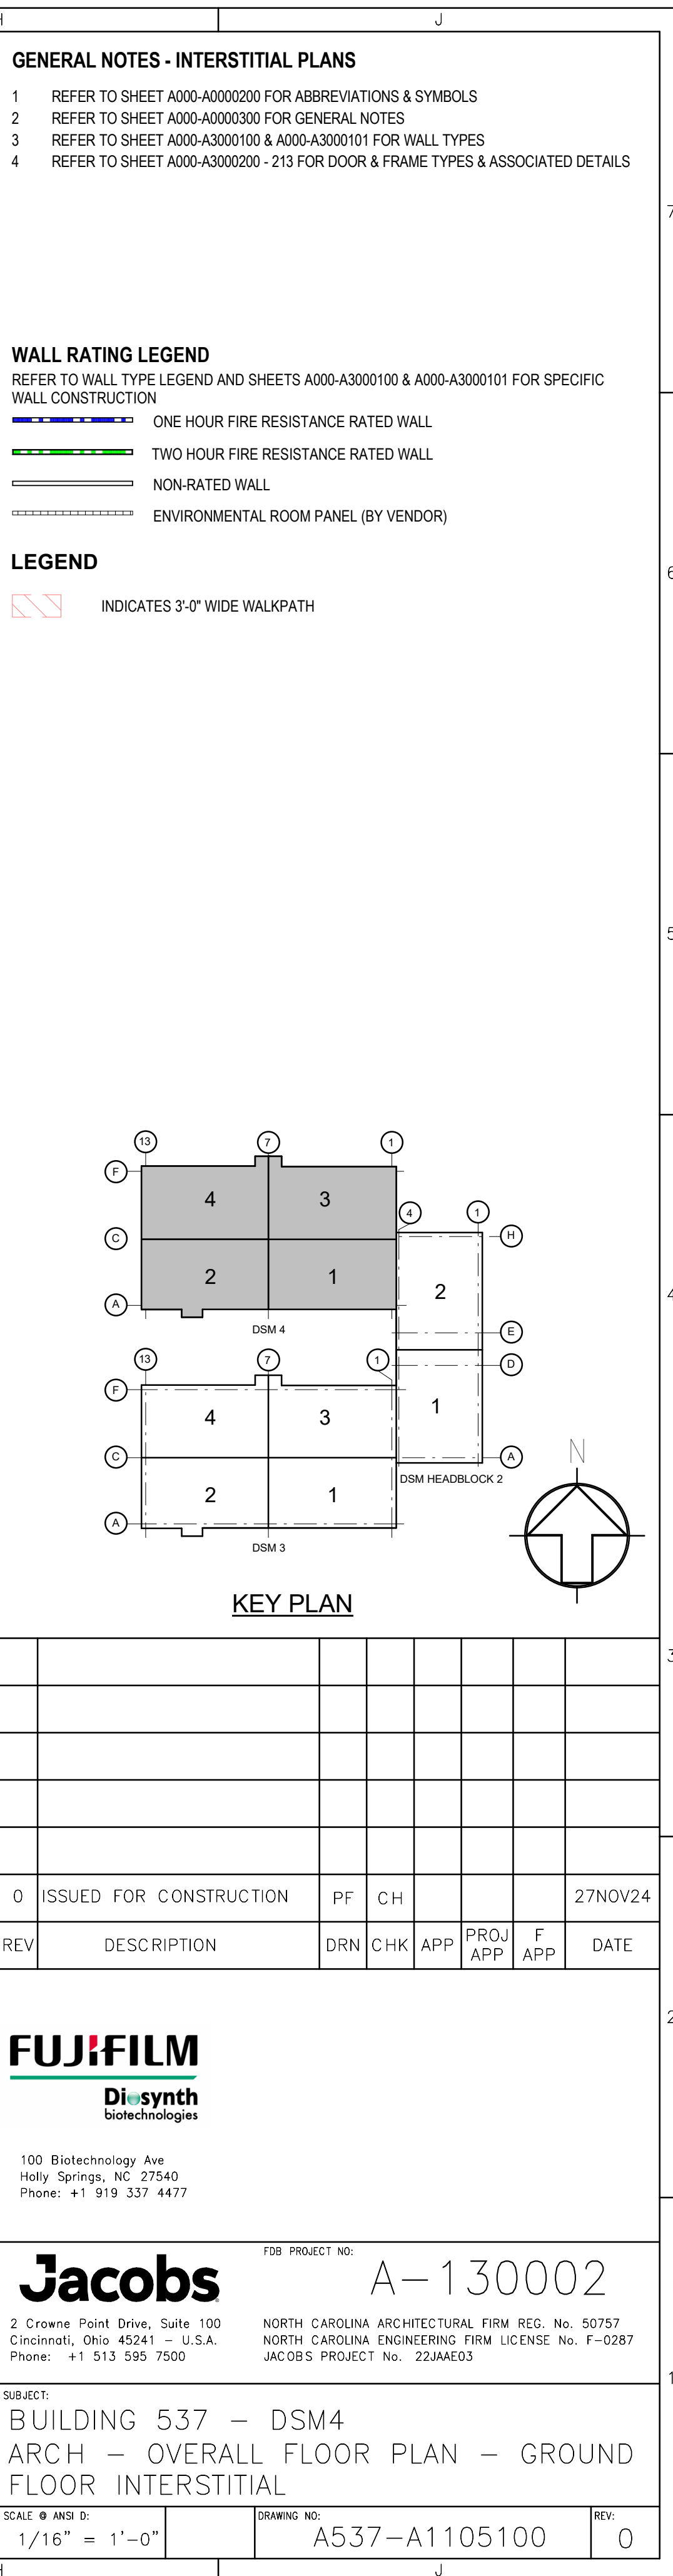


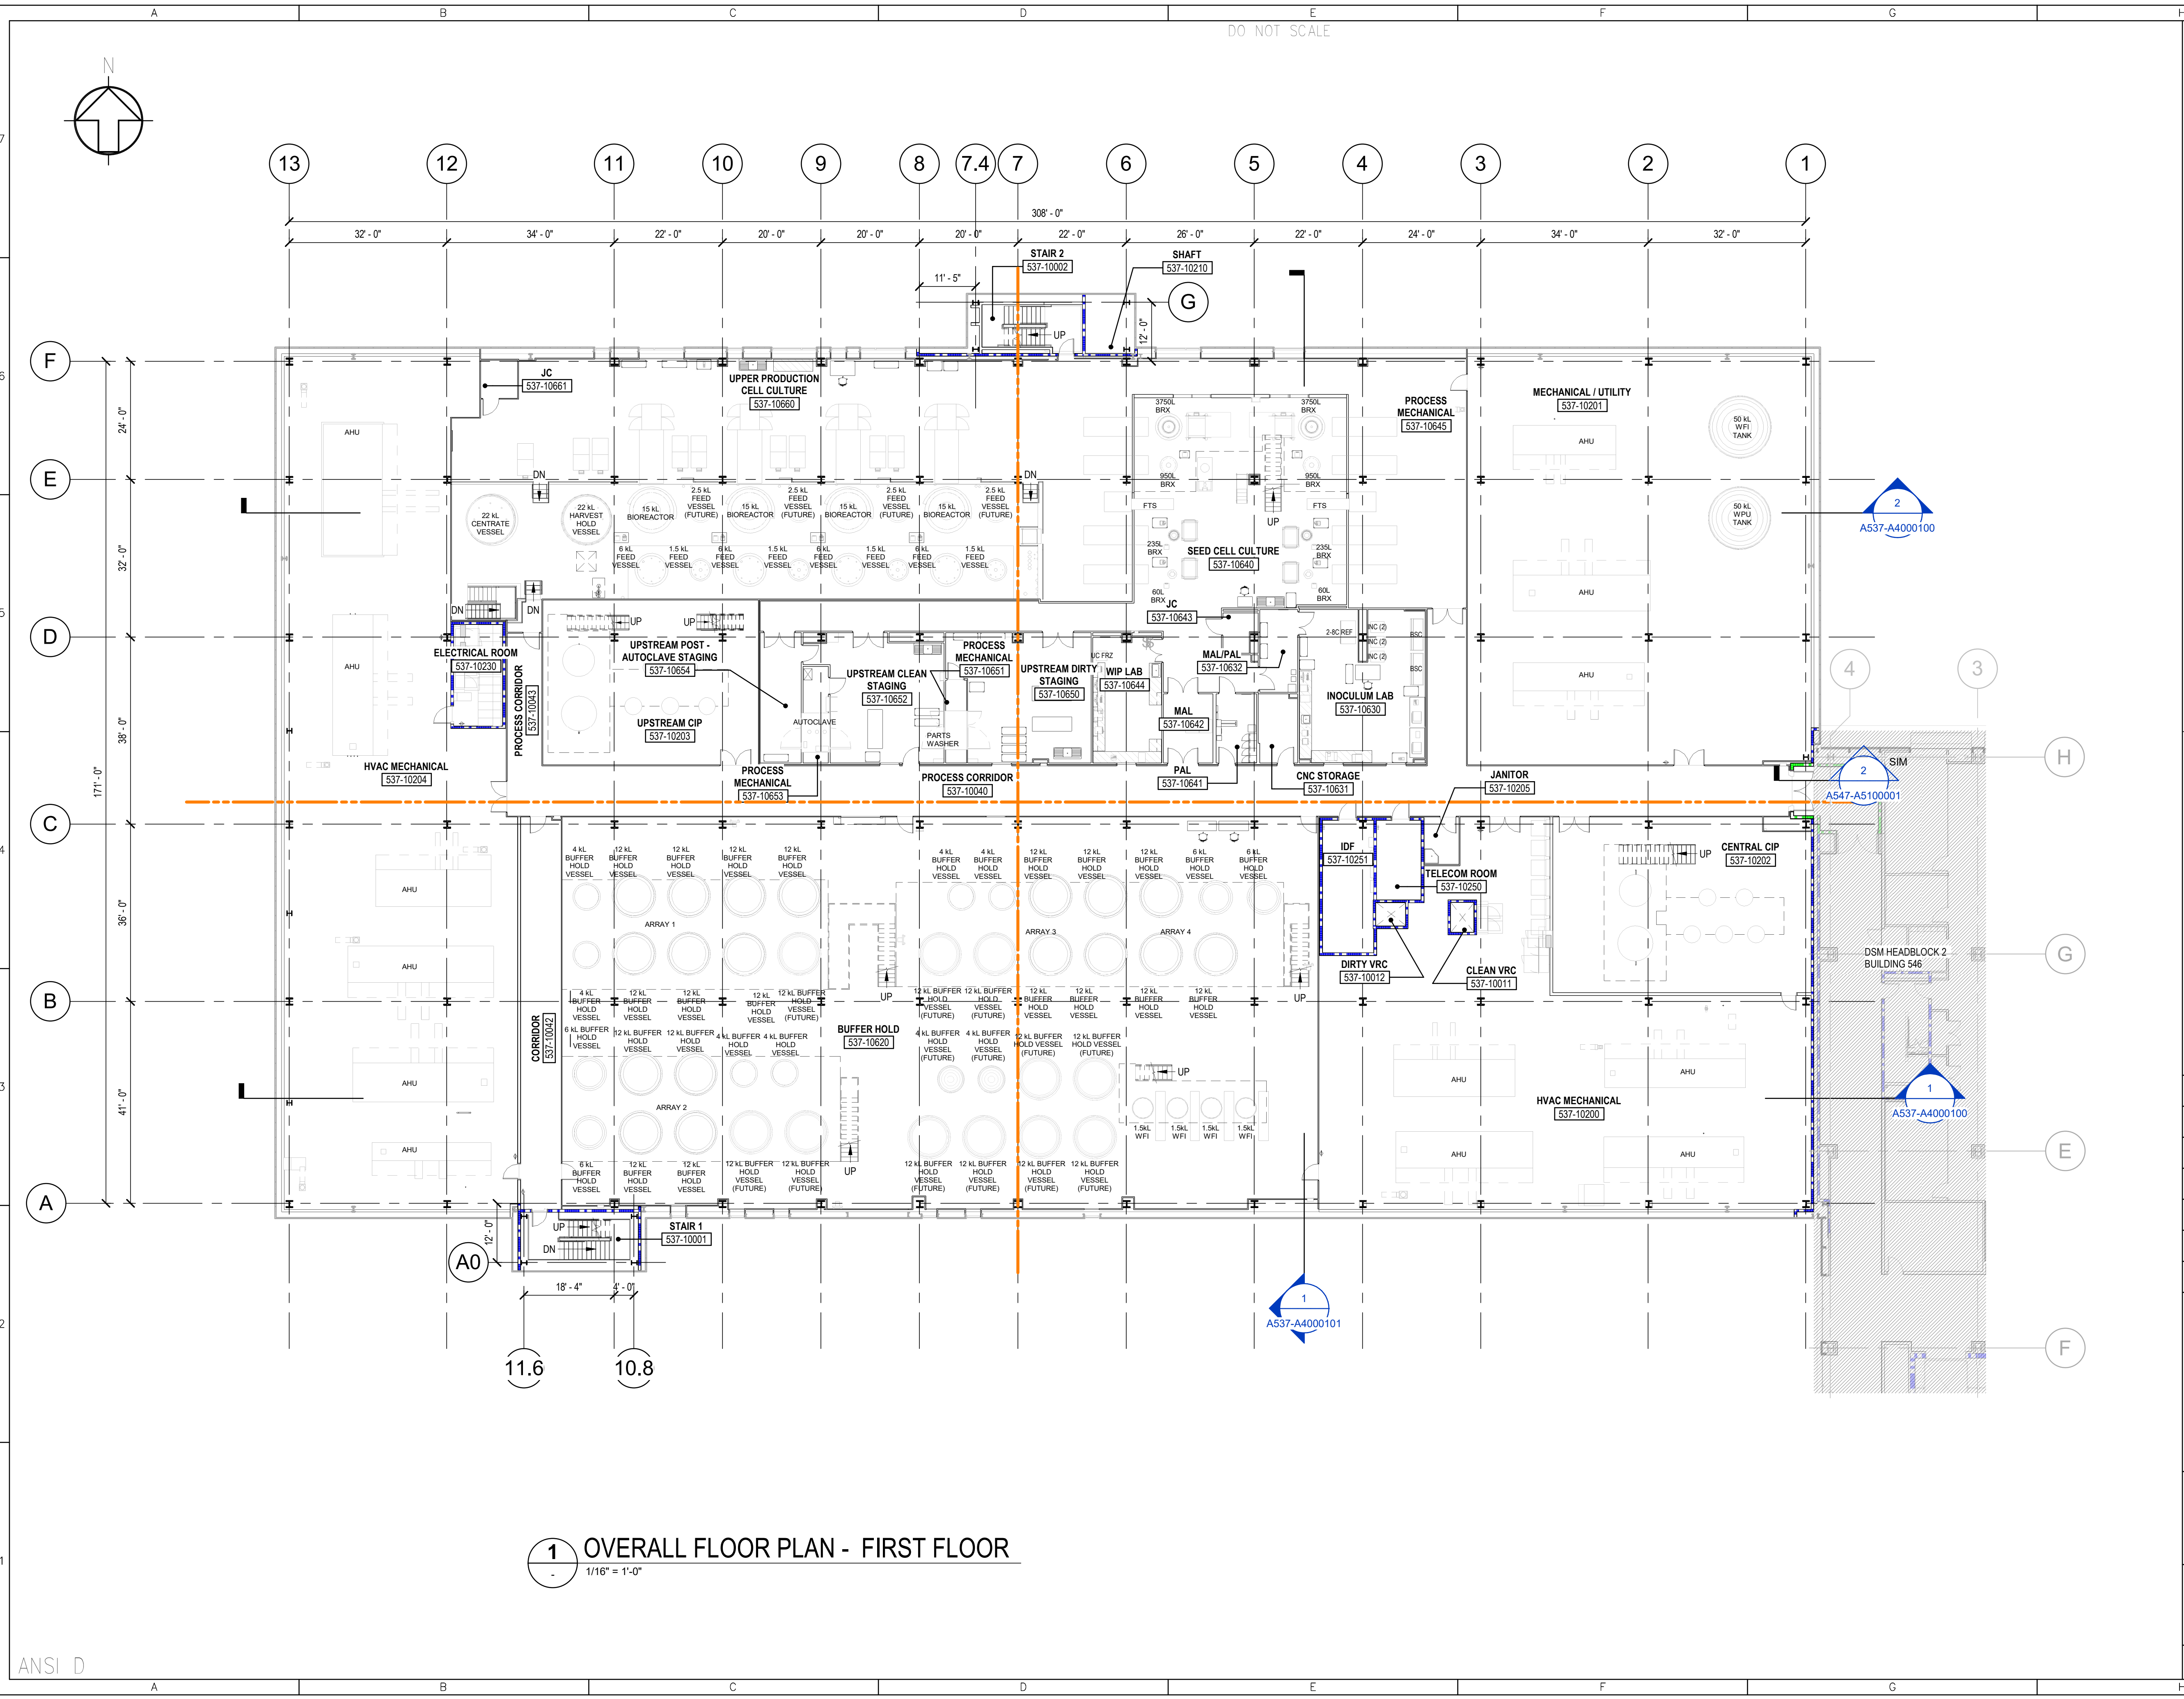

- GENERAL NOTES - FLOOR PLANS**
- 1 REFER TO SHEET A000-A0000200 FOR ABBREVIATIONS & SYMBOLS
 - 2 REFER TO SHEET A000-A0000300 FOR GENERAL NOTES
 - 3 REFER TO SHEET A000-A3000200, & 210 - 213 FOR DOOR & FRAME TYPES & ASSOCIATED DETAILS
 - 4 REFER TO SHEETS A000-A5200400 - 402 FOR TYPICAL FLOORING DETAILS, TRANSITIONS & WALL BASE CONDITIONS
 - 5 ALL DOORS 6" FROM ADJACENT WALL OR CENTERED IN WALL UNO
 - 6 REFER TO EXTERIOR CONTRACTOR DRAWINGS FOR EXTERIOR WALL SYSTEMS INFORMATION
 - 7 REFER TO CLEANROOM CONTRACTOR DRAWINGS FOR CLEANROOM AREA DIMENSIONS & DETAILS
 - 8 CONTRACTOR SHALL PROVIDE CONTINUOUS SMOKE SEALS AROUND PERIMETER OF SLABS AT EXTERIOR WALLS AND NON-RATED FLOOR SLABS AND UL APPROVED FIRE STOPPING AT PENETRATIONS THROUGH FIRE RATED SLABS AND FIRE RATED PARTITIONS. REFER TO DETAILS ON SHEETS A000-A3000120 THRU A000-A3000136.

SHEET NOTES

- WALL RATING LEGEND**
- REFER TO WALL TYPE LEGEND AND SHEETS A000-A3000100 & A000-A3000101 FOR SPECIFIC WALL CONSTRUCTION
- ONE HOUR FIRE RESISTANCE RATED WALL
 - TWO HOUR FIRE RESISTANCE RATED WALL
 - NON-RATED WALL
 - ENVIRONMENTAL ROOM PANEL (BY VENDOR)

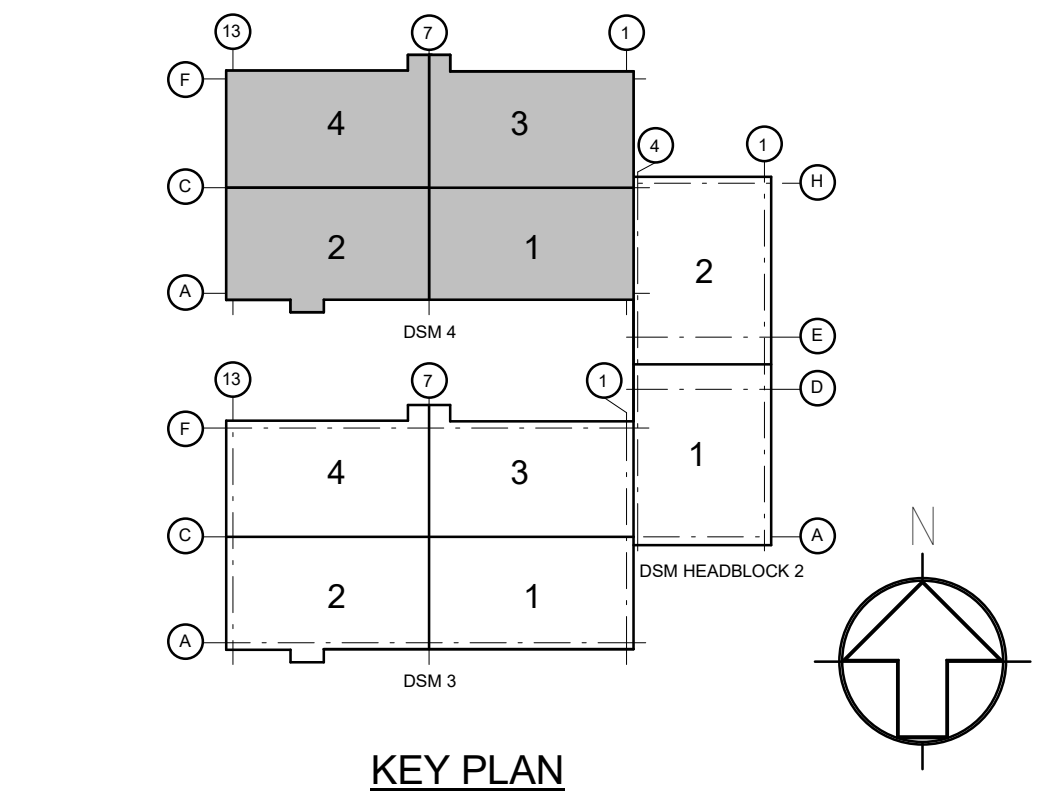

REV	DESCRIPTION	DRN	CHK	APP	PROJ APP	F APP	DATE
1	ISSUED FOR CONSTRUCTION	PF	CH				28JAN25
0	ISSUED FOR CONSTRUCTION	PF	CH				27NOV24

FUJIFILM
Di-synth
biotechnologies

100 Biotechnology Ave
Holly Springs, NC 27540
Phone: +1 919 337 4477


CHRISTOPHER HERM
REGISTERED ARCHITECT
17169
01/28/25
NORTH CAROLINA
CINCINNATI, OH

Jacobs FCB PROJECT NO: A-130002

2 Crowne Point Drive, Suite 100
Cincinnati, Ohio 45241 - U.S.A.
Phone: +1 513 595 7500

NORTH CAROLINA ARCHITECTURAL FIRM REG. No. 50757
NORTH CAROLINA ENGINEERING FIRM LICENSE No. F-0287
JACOBS PROJECT No. 22JAAE03

SUBJECT: BUILDING 537 - DSM4 ARCH - OVERALL FLOOR PLAN - FIRST FLOOR						
SCALE @ ANSI D: 1/16" = 1'-0"	DRAWING NO: A537-A1110100	REV: 1				

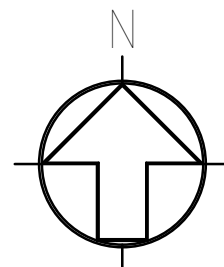

DO NOT SCALE

GENERAL NOTES - INTERSTITIAL PLANS

- 1 REFER TO SHEET A000-A0000200 FOR ABBREVIATIONS & SYMBOLS
- 2 REFER TO SHEET A000-A0000300 FOR GENERAL NOTES
- 3 REFER TO SHEET A000-A3000100 & A000-A3000101 FOR WALL TYPES
- 4 REFER TO SHEET A000-A3000200 - 213 FOR DOOR & FRAME TYPES & ASSOCIATED DETAILS


WALL RATING LEGEND

REFER TO WALL TYPE LEGEND AND SHEETS A000-A3000100 & A000-A3000101 FOR SPECIFIC WALL CONSTRUCTION

- ONE HOUR FIRE RESISTANCE RATED WALL
- TWO HOUR FIRE RESISTANCE RATED WALL
- NON-RATED WALL
- ENVIRONMENTAL ROOM PANEL (BY VENDOR)

LEGEND

- INDICATES 3'-0" WIDE WALKPATH

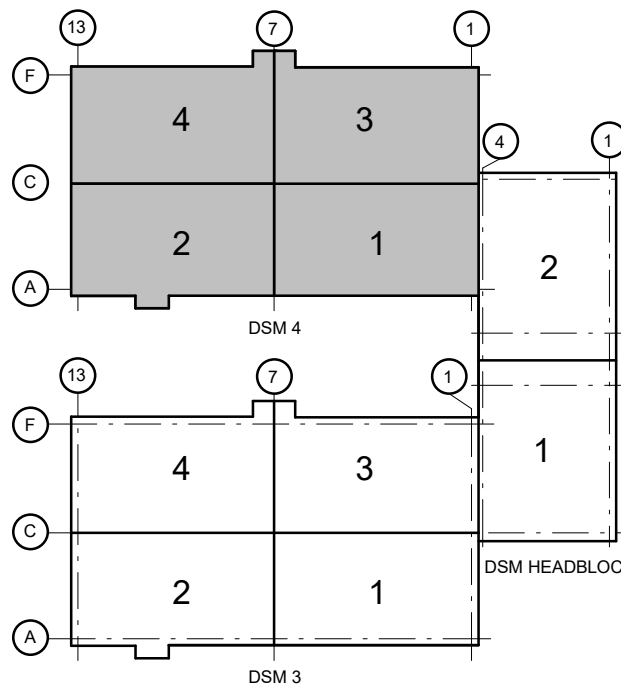

KEY PLAN

0	ISSUED FOR CONSTRUCTION	PF	CH			27NOV24
REV	DESCRIPTION	DRN	CHK	APP	PROJ APP	F APP DATE



100 Biotechnology Ave
Holly Springs, NC 27540
Phone: +1 919 337 4477



FDB PROJECT NO: A-130002

2 Crowne Point Drive, Suite 100
Cincinnati, Ohio 45241 - U.S.A.
Phone: +1 513 595 7500

NORTH CAROLINA ARCHITECTURAL FIRM REG. No. 50757
NORTH CAROLINA ENGINEERING FIRM LICENSE No. F-0287
JACOBS PROJECT No. 22JAAE03

SUBJECT:
BUILDING 537 - DSM4
ARCH - OVERALL FLOOR PLAN - FIRST FLOOR INTERSTITIAL

SCALE @ ANSI D:
1/16" = 1'-0"

DRAWING NO:
A537-A1115100

REV:
0

1 OVERALL FLOOR PLAN - DSM FIRST FLOOR INTERSTITIAL

1/16" = 1'-0"

ANSI D



GENERAL NOTES - FLOOR PLANS


- 1 REFER TO SHEET A000-A0000200 FOR ABBREVIATIONS & SYMBOLS
- 2 REFER TO SHEET A000-A0000300 FOR GENERAL NOTES
- 3 REFER TO SHEET A000-A3000200, & 210 - 213 FOR DOOR & FRAME TYPES & ASSOCIATED DETAILS
- 4 REFER TO SHEETS A000-A5200400 - 402 FOR TYPICAL FLOORING DETAILS, TRANSITIONS WALL BASE CONDITIONS
- 5 ALL DOORS 6" FROM ADJACENT WALL OR CENTERED IN WALL UNO
- 6 REFER TO EXTERIOR CONTRACTOR DRAWINGS FOR EXTERIOR WALL SYSTEMS INFORMATION
- 7 REFER TO CLEANROOM CONTRACTOR DRAWINGS FOR CLEANROOM AREA DIMENSIONS DETAILS
- 8 CONTRACTOR SHALL PROVIDE CONTINUOUS SMOKE SEALS AROUND PERIMETER OF SLABS AT EXTERIOR WALLS AND NON-RATED FLOOR SLABS AND UL APPROVED FIRE STOPPING AT PENETRATIONS THROUGH FIRE RATED SLABS AND FIRE RATED PARTITIONS. REFER TO DETAILS ON SHEETS A000-A3000120 THRU A000-A3000136.

SHEET NOTES:

WALL RATING LEGEND

REFER TO WALL TYPE LEGEND AND SHEETS A000-A3000100 & A000-A3000101 FOR SPECIFIC WALL CONSTRUCTION

	ONE HOUR FIRE RESISTANCE RATED WALL
	TWO HOUR FIRE RESISTANCE RATED WALL
	NON-RATED WALL
	ENVIRONMENTAL ROOM PANEL (BY VENDOR)

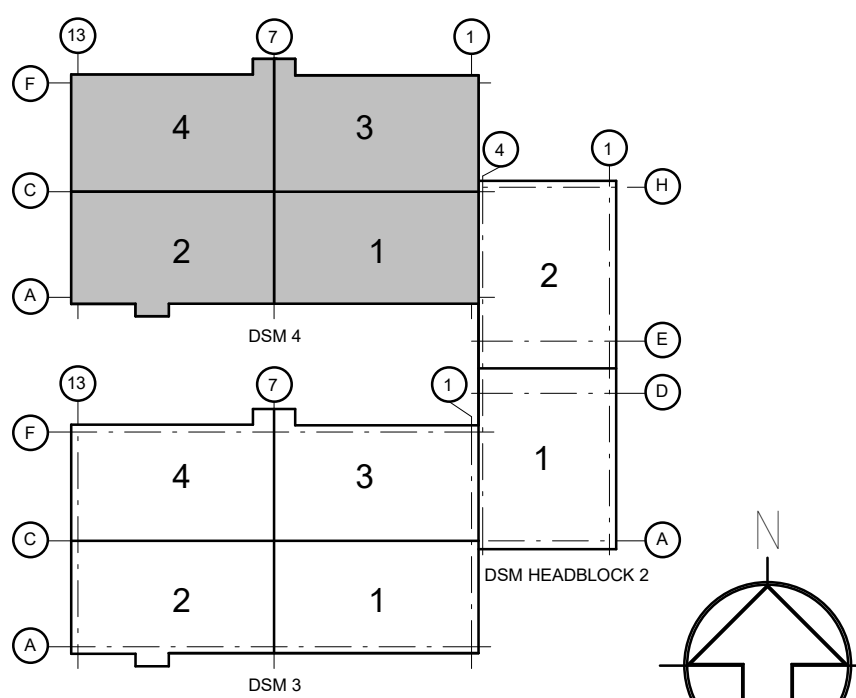


KEY PLAN

1	ISSUED FOR CONSTRUCTION	PF	CH					28JAN
0	ISSUED FOR CONSTRUCTION	PF	CH					27NOV
REV	DESCRIPTION	DRN	CHK	APP	PROJ APP	F APP		DATE



100 Biotechnology Ave
Holly Springs, NC 27540
Phone: +1 919 337 4477

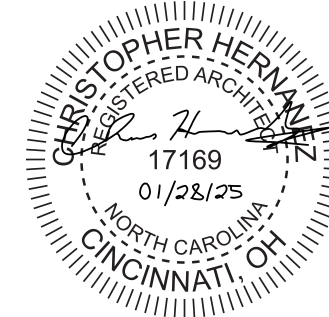

Jacobs

2 Crowne Point Drive, Suite 100
Cincinnati, Ohio 45241 - U.S.A.
Phone: +1 513 595 7500

FDB PROJECT NO:

A-130002

NORTH CAROLINA ARCHITECTURAL FIRM REG. No. 50757
NORTH CAROLINA ENGINEERING FIRM LICENSE No. F-028
JACOBS PROJECT No. 22JAAE03

SUBJECT:


BUILDING 537 - DSM4
ARCH - OVERALL FLOOR PLAN - SECOND
FLOOR

SCALE ☒ ANSI D:
1/16" =

DRAWING NO:

A537-A1120100


REV:

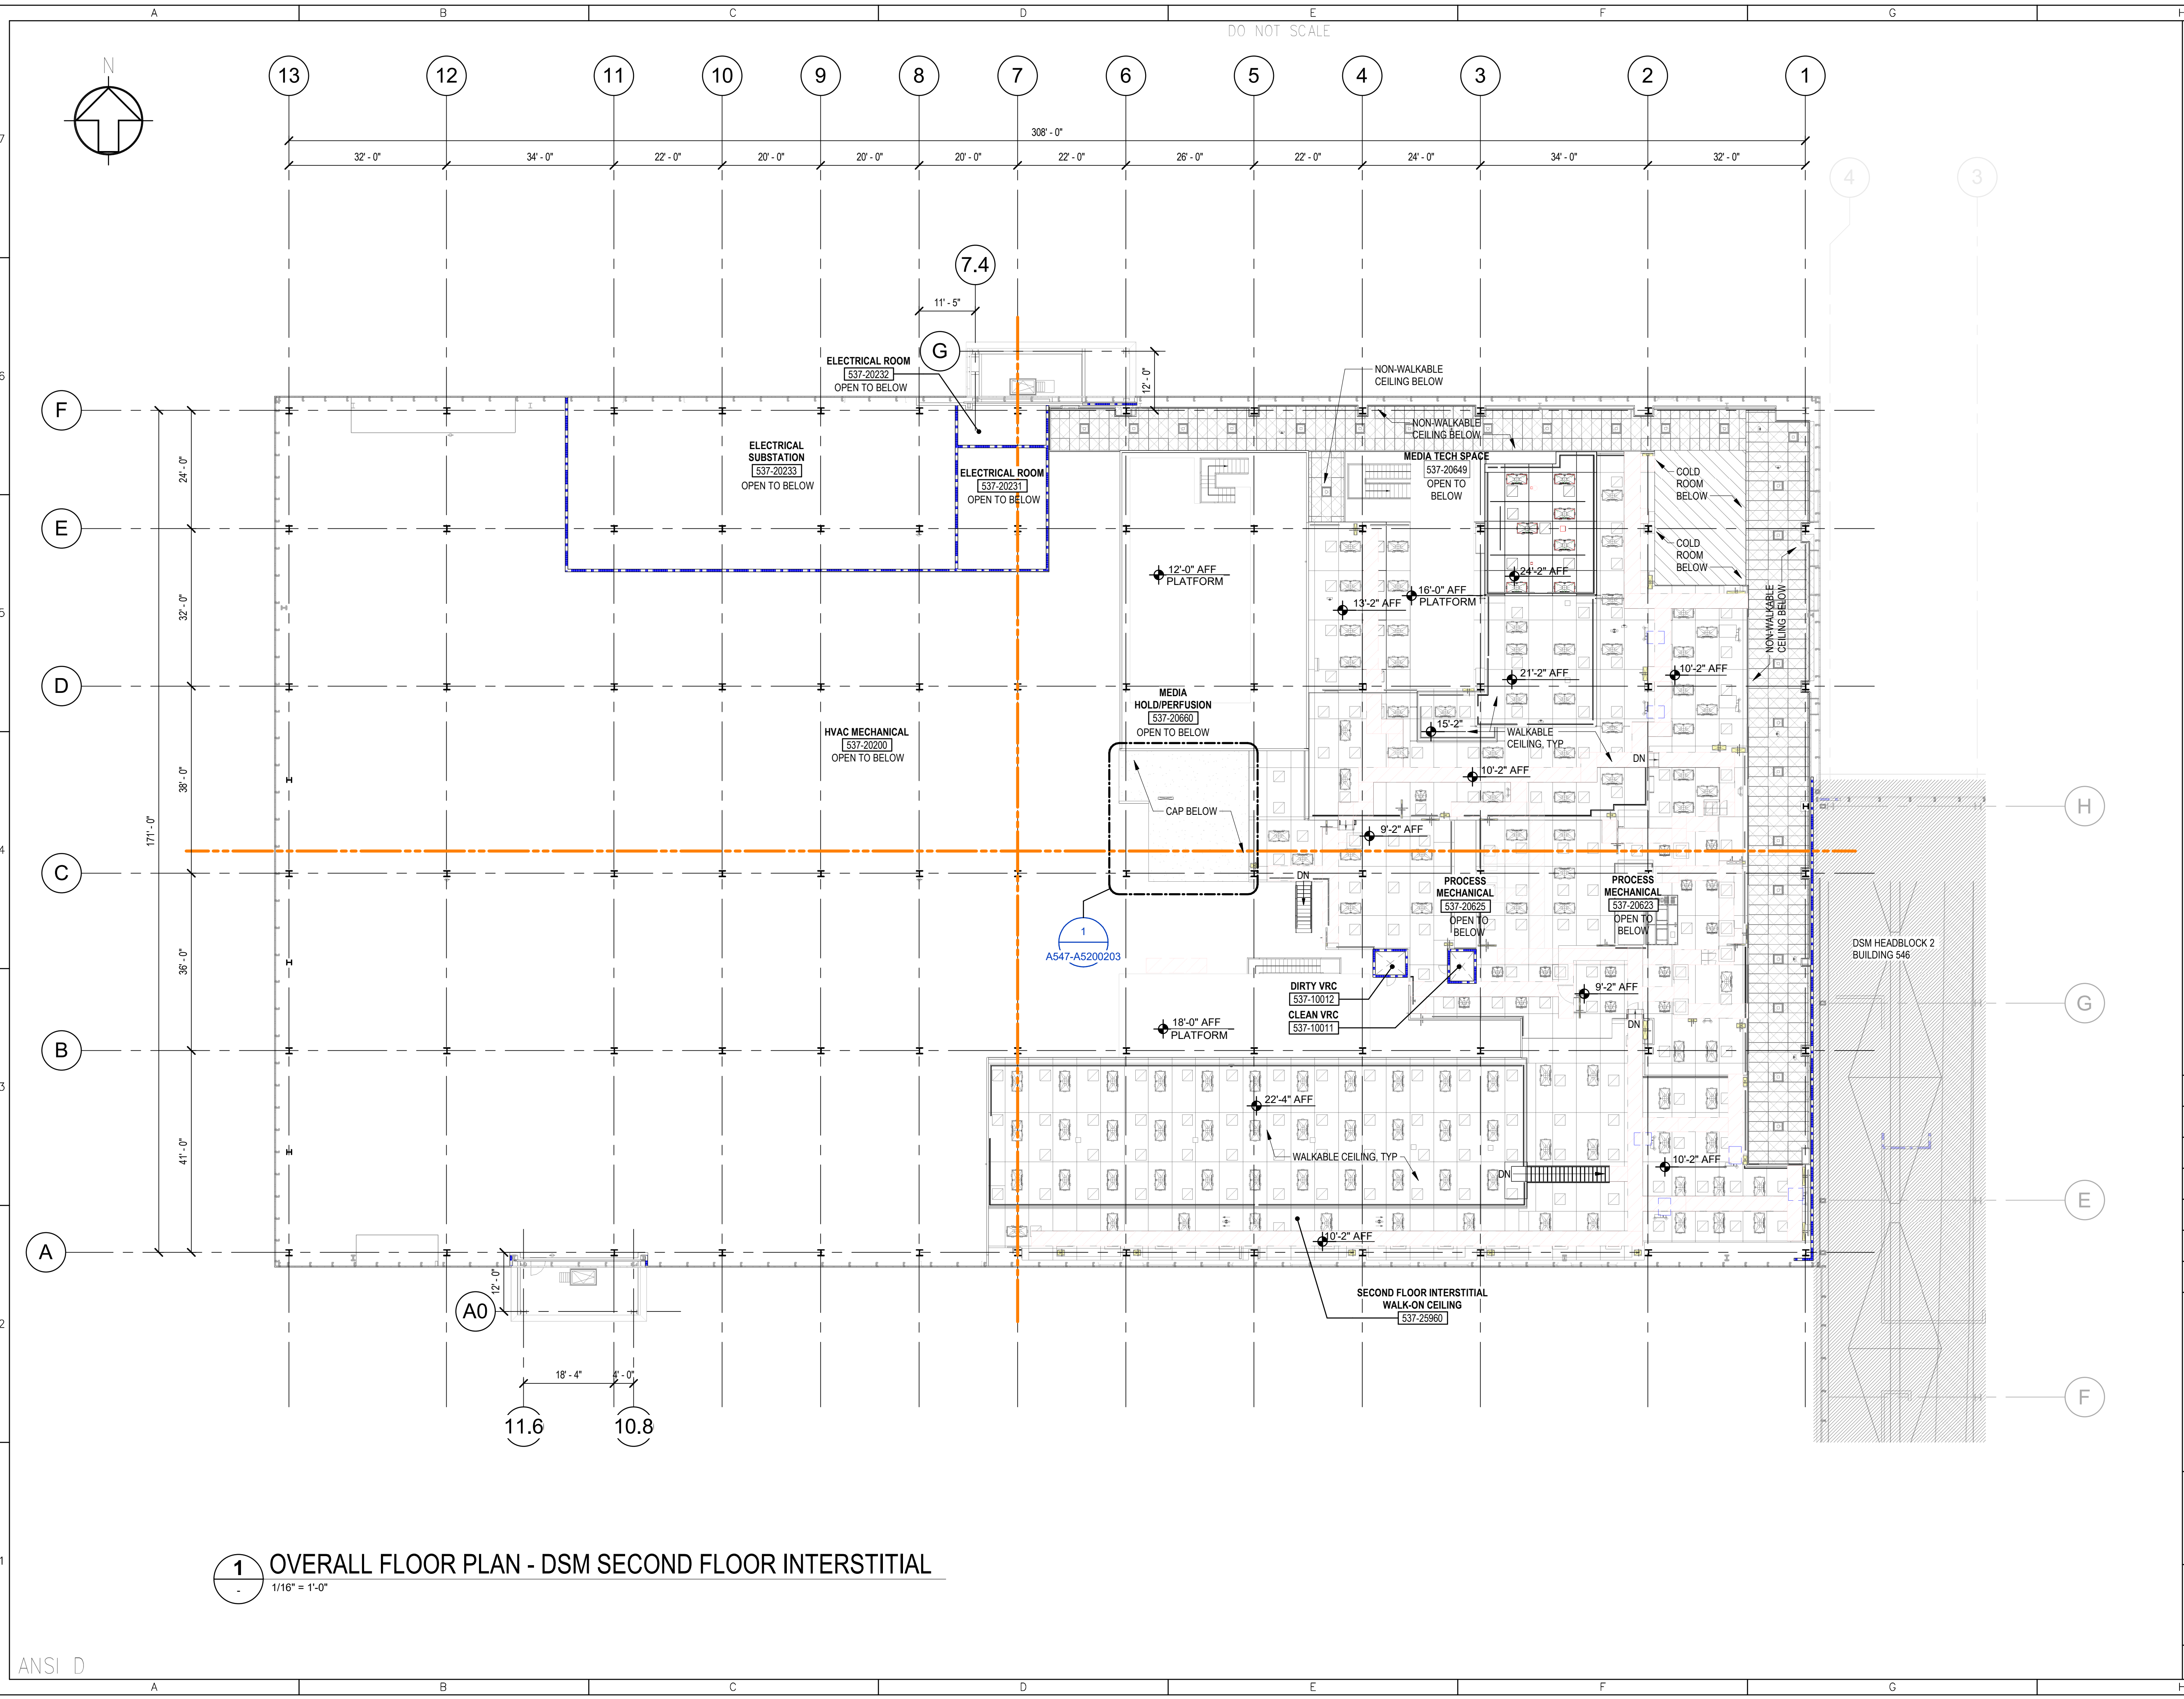

- GENERAL NOTES - INTERSTITIAL PLANS**
- REFER TO SHEET A000-A0000200 FOR ABBREVIATIONS & SYMBOLS
 - REFER TO SHEET A000-A0000300 FOR GENERAL NOTES
 - REFER TO SHEET A000-A3000100 & A000-A3000101 FOR WALL TYPES
 - REFER TO SHEET A000-A3000200 - 213 FOR DOOR & FRAME TYPES & ASSOCIATED DETAILS

- WALL RATING LEGEND**
- REFER TO WALL TYPE LEGEND AND SHEETS A000-A3000100 & A000-A3000101 FOR SPECIFIC WALL CONSTRUCTION
- ONE HOUR FIRE RESISTANCE RATED WALL
 - TWO HOUR FIRE RESISTANCE RATED WALL
 - NON-RATED WALL
 - ENVIRONMENTAL ROOM PANEL (BY VENDOR)

- LEGEND**
- INDICATES 3'-0" WIDE WALKPATH

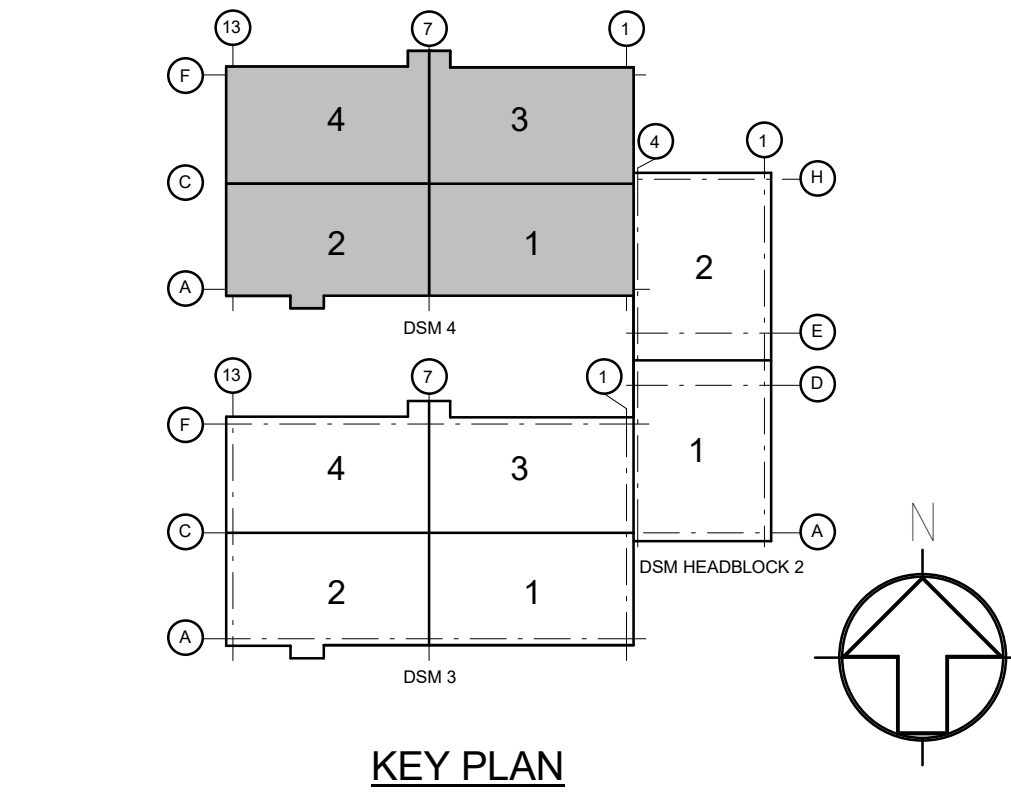

0	ISSUED FOR CONSTRUCTION	PF	CH			27NOV24
REV	DESCRIPTION	DRN	CHK	APP	PROJ APP	F APP DATE

FUJIFILM

Disynth
biotechnologies

100 Biotechnology Ave
Holly Springs, NC 27540
Phone: +1 919 337 4477

Jacobs

2 Crowne Point Drive, Suite 100
Cincinnati, Ohio 45241 - U.S.A.
Phone: +1 513 595 7500

NORTH CAROLINA ARCHITECTURAL FIRM REG. No. 50757
NORTH CAROLINA ENGINEERING FIRM LICENSE No. F-0287
JACOBS PROJECT No. 22JAAE03

FDB PROJECT NO:

A-130002

SUBJECT:

BUILDING 537 - DSM4
ARCH - OVERALL FLOOR PLAN - SECOND FLOOR INTERSTITIAL

SCALE @ ANSI D:
1/16" = 1'-0"

DRAWING NO:
A537-A1125100

REV:
0

1 OVERALL FLOOR PLAN - DSM SECOND FLOOR INTERSTITIAL
1/16" = 1'-0"